
J ANGLE STUDIO
ARCHITECTURE & INTERIORS

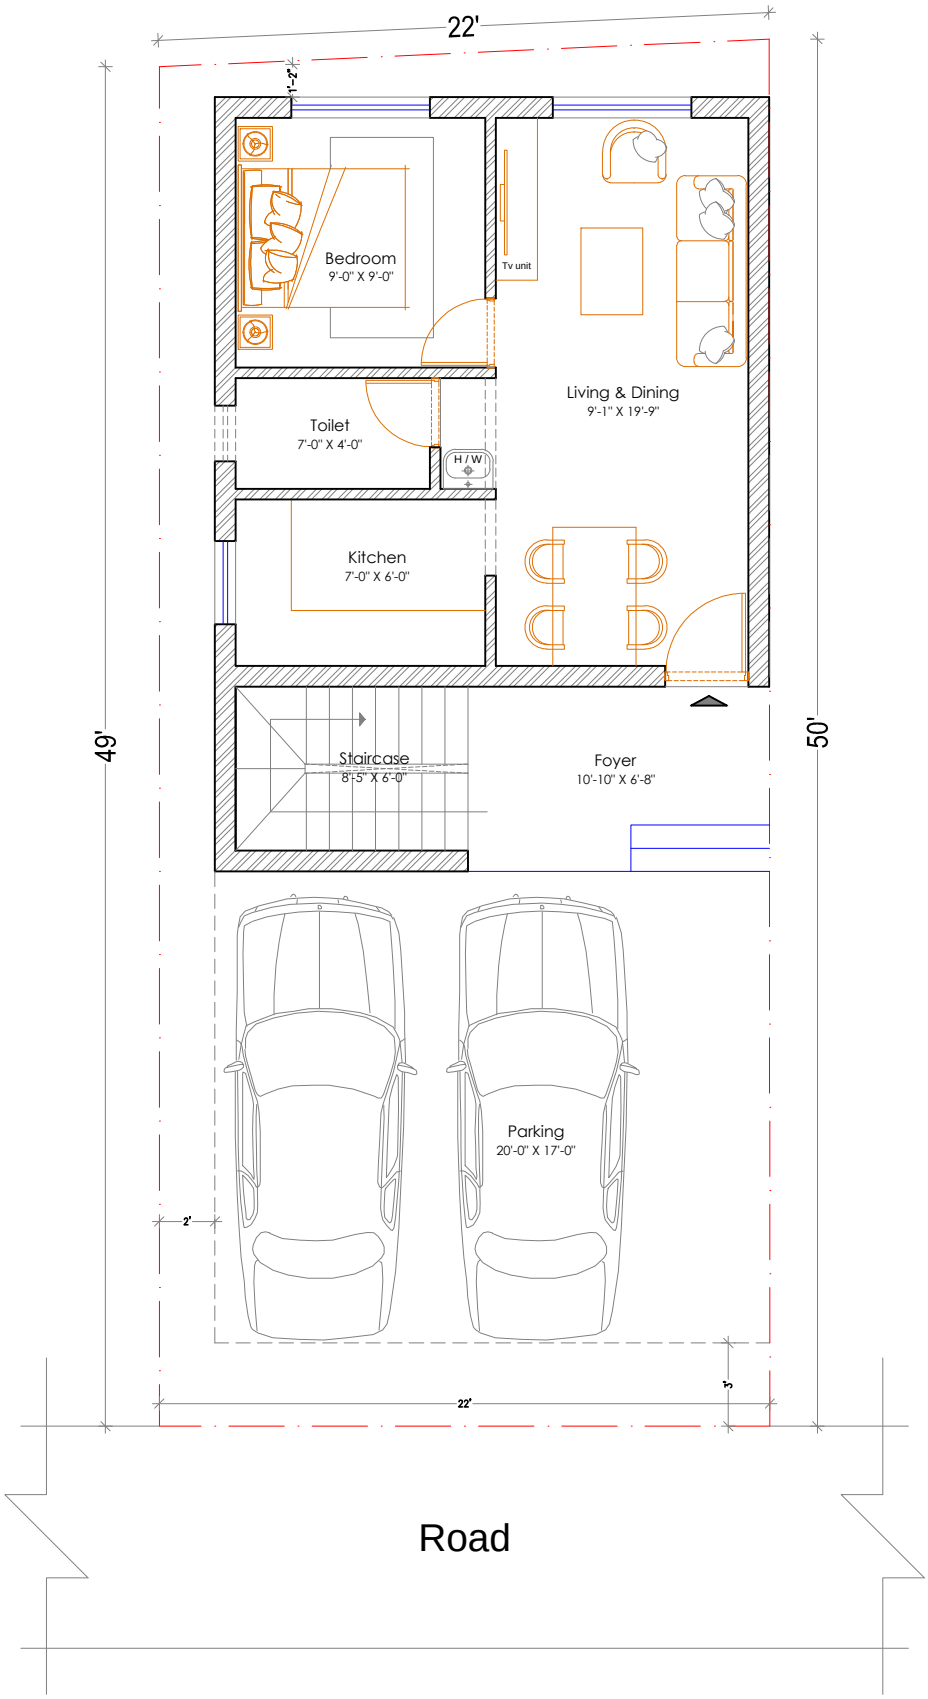

JOB TITLE	STRUCTURAL AND CONTRACTOR	LANDSCAPE CONSULTANT	ARCHITECTURAL CONSULTANT
PROPOSED RESIDENCE AT GUINDY, CHENNAI			
	ELECTRICAL CONSULTANT	PLUMBING CONSULTANT	DRAWING STATUS: SCHEME — NORTH

REVISIONS

SL.NO.	DATE	REVISION	SIGN

NOTES


1. All dimensions are in Feet and inches system.
2. Drawings should not be scaled for obtaining dimensions.
3. If any discrepancy is found in the drawing it is to be brought to the notice of the Architect before execution of work at site.
4. This drawing is to be read along with the structural/ electrical/sanitary/plumbing and other related drawings.
5. This drawing is the property of J-angle studio, Chennai . No copying / reproduction of this drawing by any method shall be done without the permission of the owner.

DRAWING TITLE: SITE / GROUND FLOOR SCHEME

DRAWING NO: 145/GUINDY RESIDENCE/ARCH/SCH-01A

DRAWN : SHARAN	DATE : 24.04.2026
CHECKED : JANARTHANAN	SCALE : N.T.S
JOB NO. : ---	REV. NO. : R1
FILE LOCATION : ----------	

J - ANGLE STUDIO
ARCHITECTURE I INTERIOR DESIGN I LANDSCAPE
Plot No.54, Door no. FF-2, First Floor, Anna Nagar 2nd Street,
Tansi Nagar, Velachery, Chennai - 600042
E-mail - janglestudio@gmail.com I Phone - 9841424267 / 8072113728

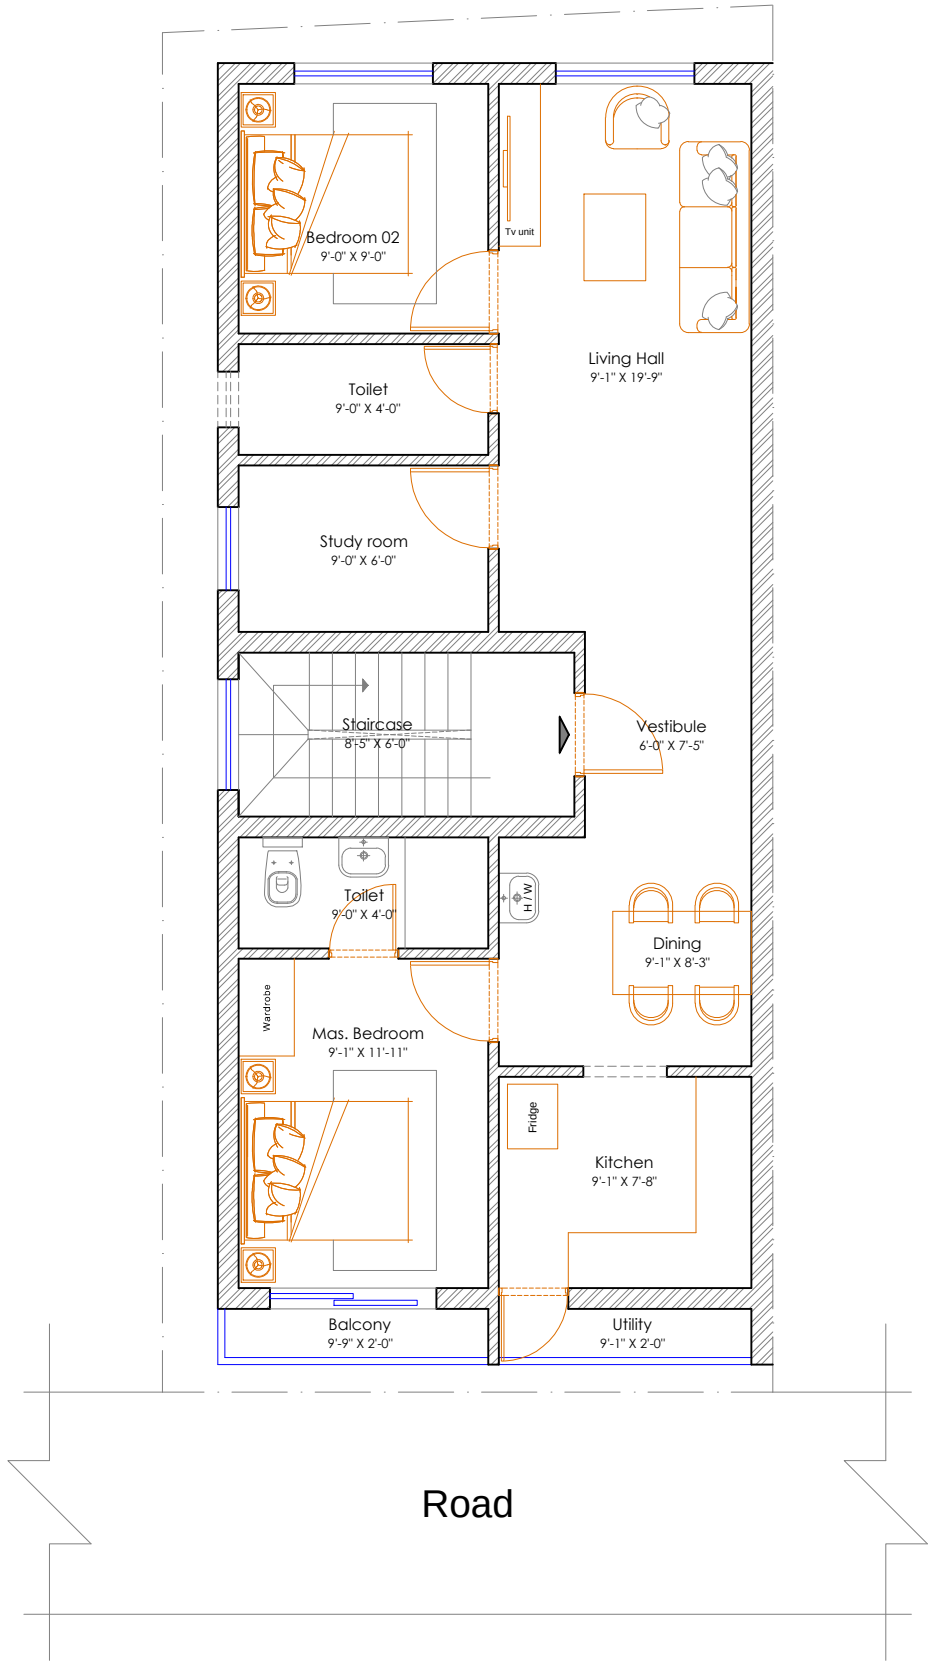

JOB TITLE	STRUCTURAL AND CONTRACTOR	LANDSCAPE CONSULTANT	ARCHITECTURAL CONSULTANT
PROPOSED RESIDENCE AT GUINDY, CHENNAI			
	ELECTRICAL CONSULTANT	PLUMBING CONSULTANT	DRAWING STATUS: SCHEME / NORTH

REVISIONS

SL.NO.	DATE	REVISION	SIGN

NOTES

1. All dimensions are in Feet and inches system.
2. Drawings should not be scaled for obtaining dimensions.
3. If any discrepancy is found in the drawing it is to be brought to the notice of the Architect before execution of work at site.
4. This drawing is to be read along with the structural/ electrical/sanitary/plumbing and other related drawings.
5. This drawing is the property of J-angle studio, Chennai . No copying / reproduction of this drawing by any method shall be done without the permission of the owner.

DRAWING TITLE: FIRST FLOOR SCHEME

DRAWING NO: 145/GUINDY RESIDENCE/ARCH/SCH-01A

DRAWN : SHARAN	DATE : 24.04.2026
CHECKED : JANARTHANAN	SCALE : N.T.S
JOB NO. : ---	REV. NO. : R1

FILE LOCATION : ----------

J - ANGLE STUDIO
ARCHITECTURE I INTERIOR DESIGN I LANDSCAPE
Plot No.54, Door no. FF-2, First Floor, Anna Nagar 2nd Street,
Tansi Nagar, Velachery, Chennai - 600042
E-mail - janglestudio@gmail.com I Phone - 9841424267 / 8072113728